



## ROZMIESTNENIE NÁBYTKU KNIŽNICA - 21 06 2017 - A

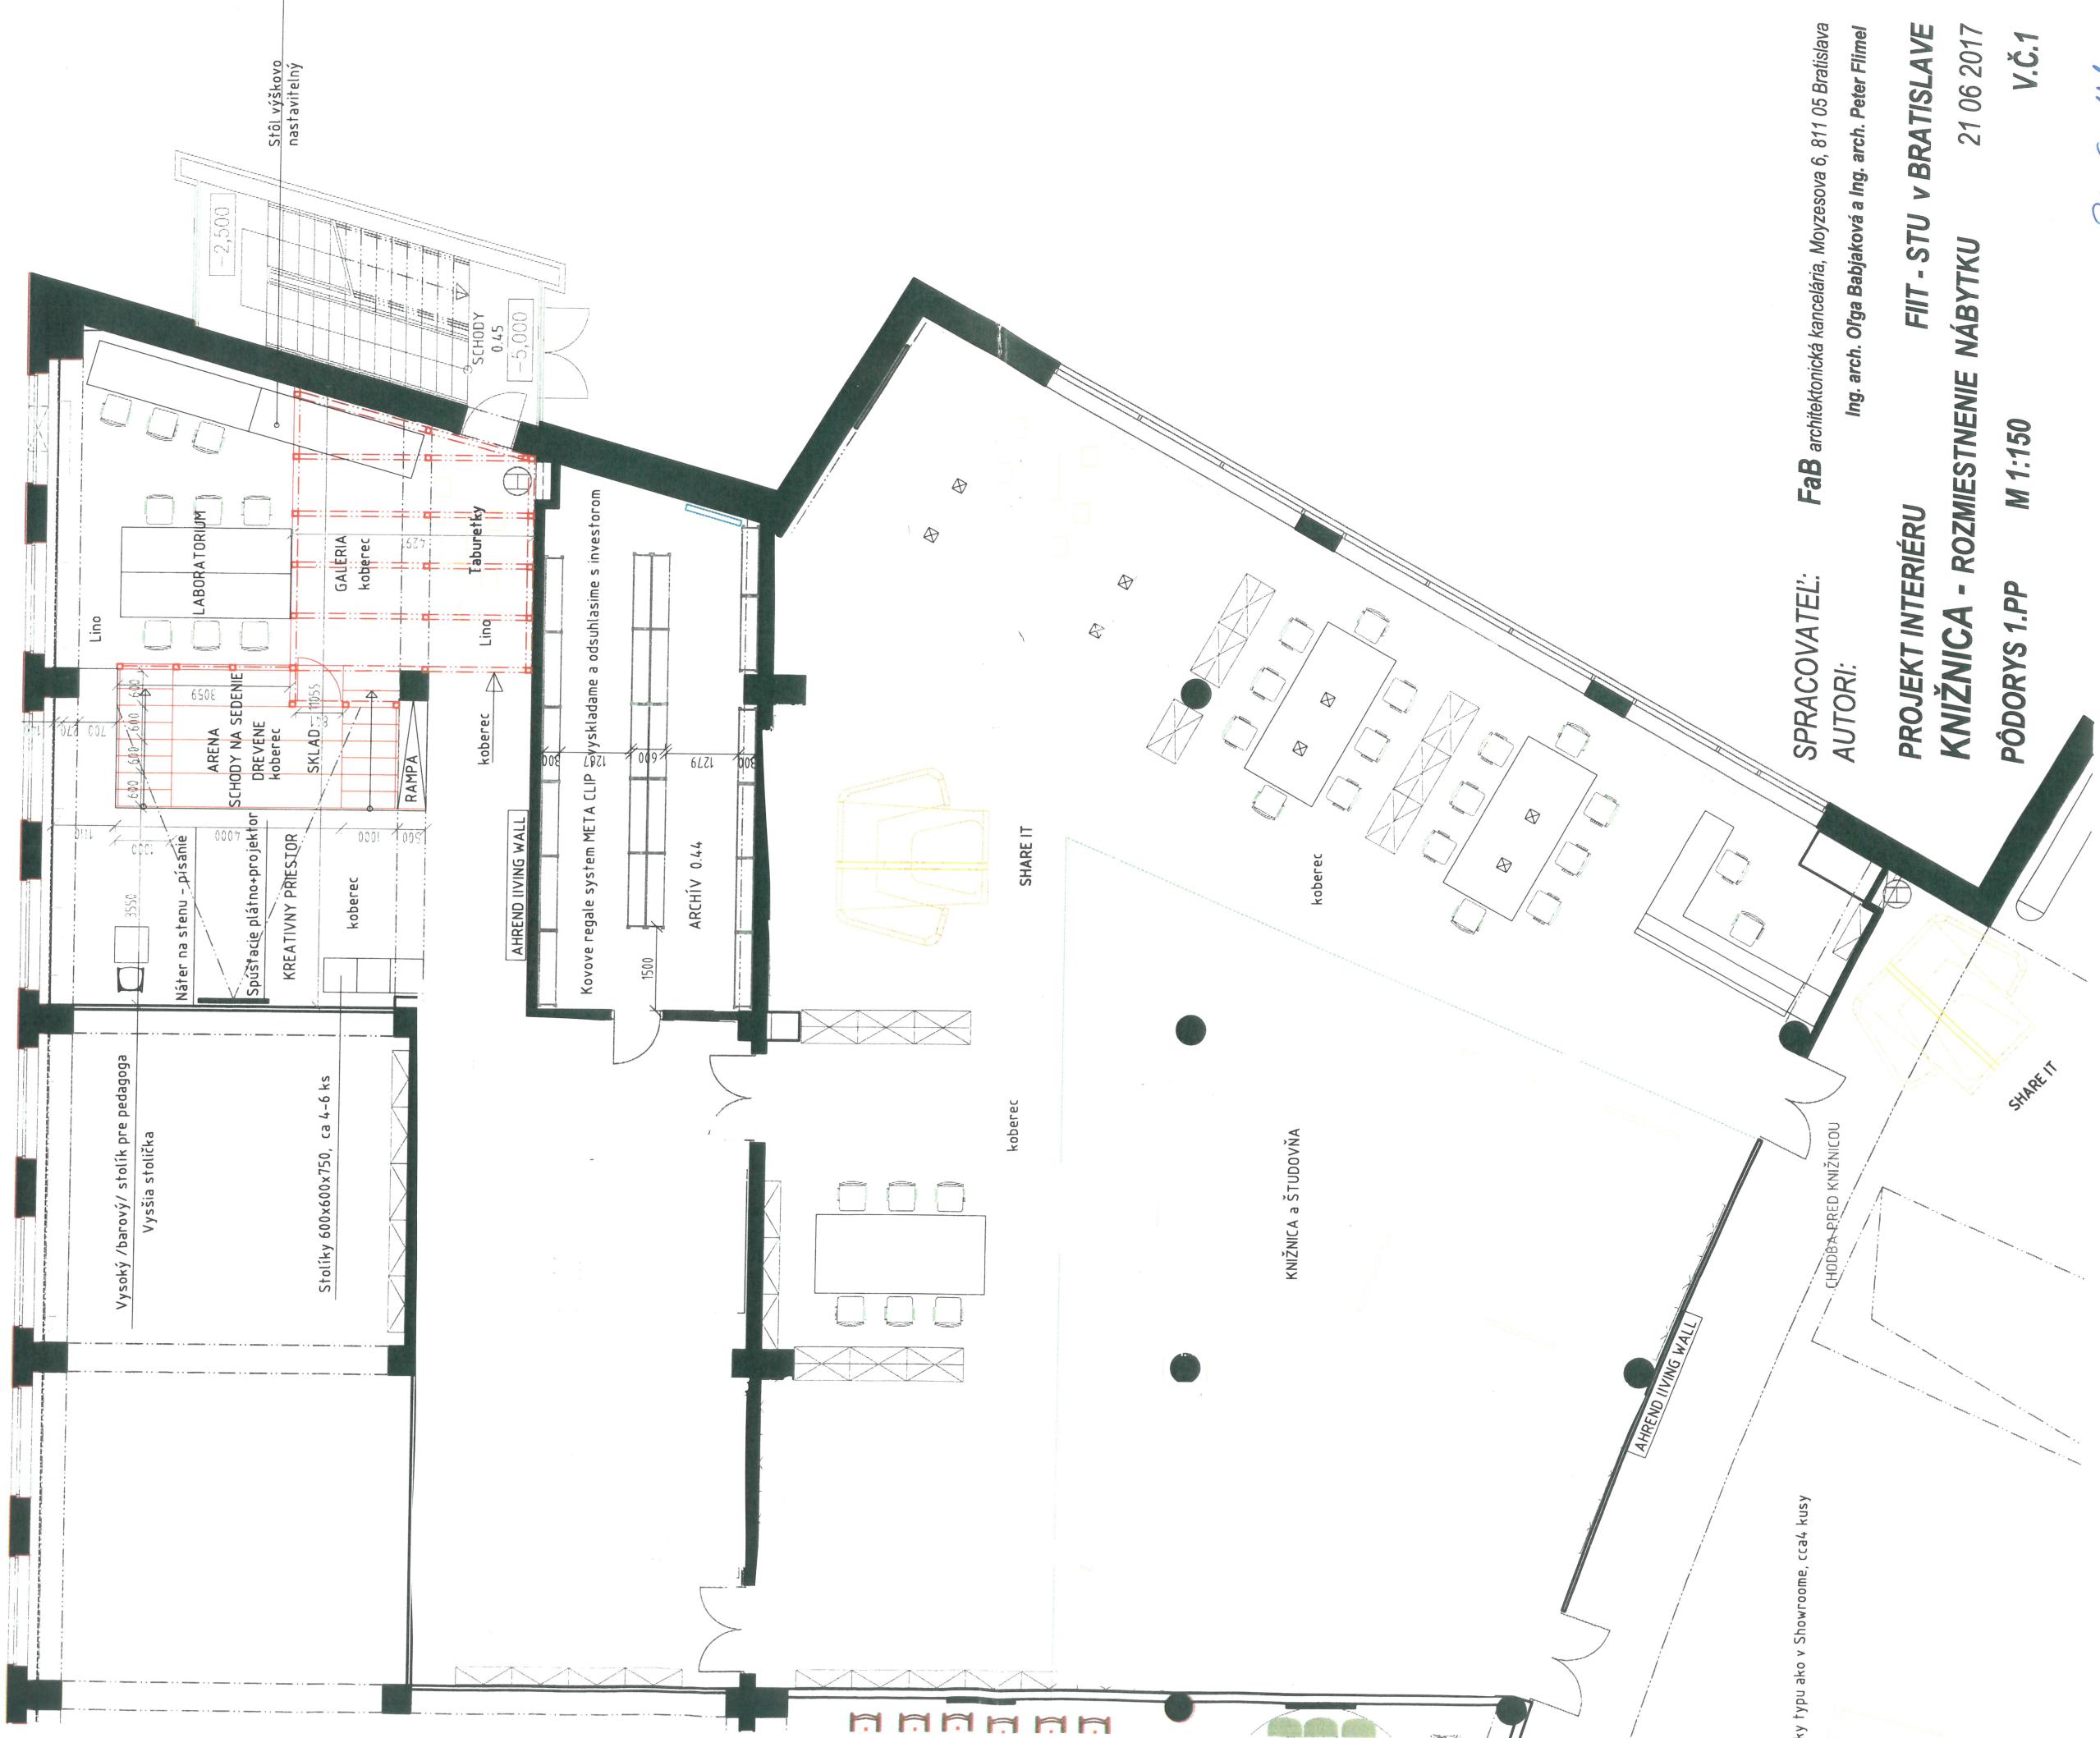

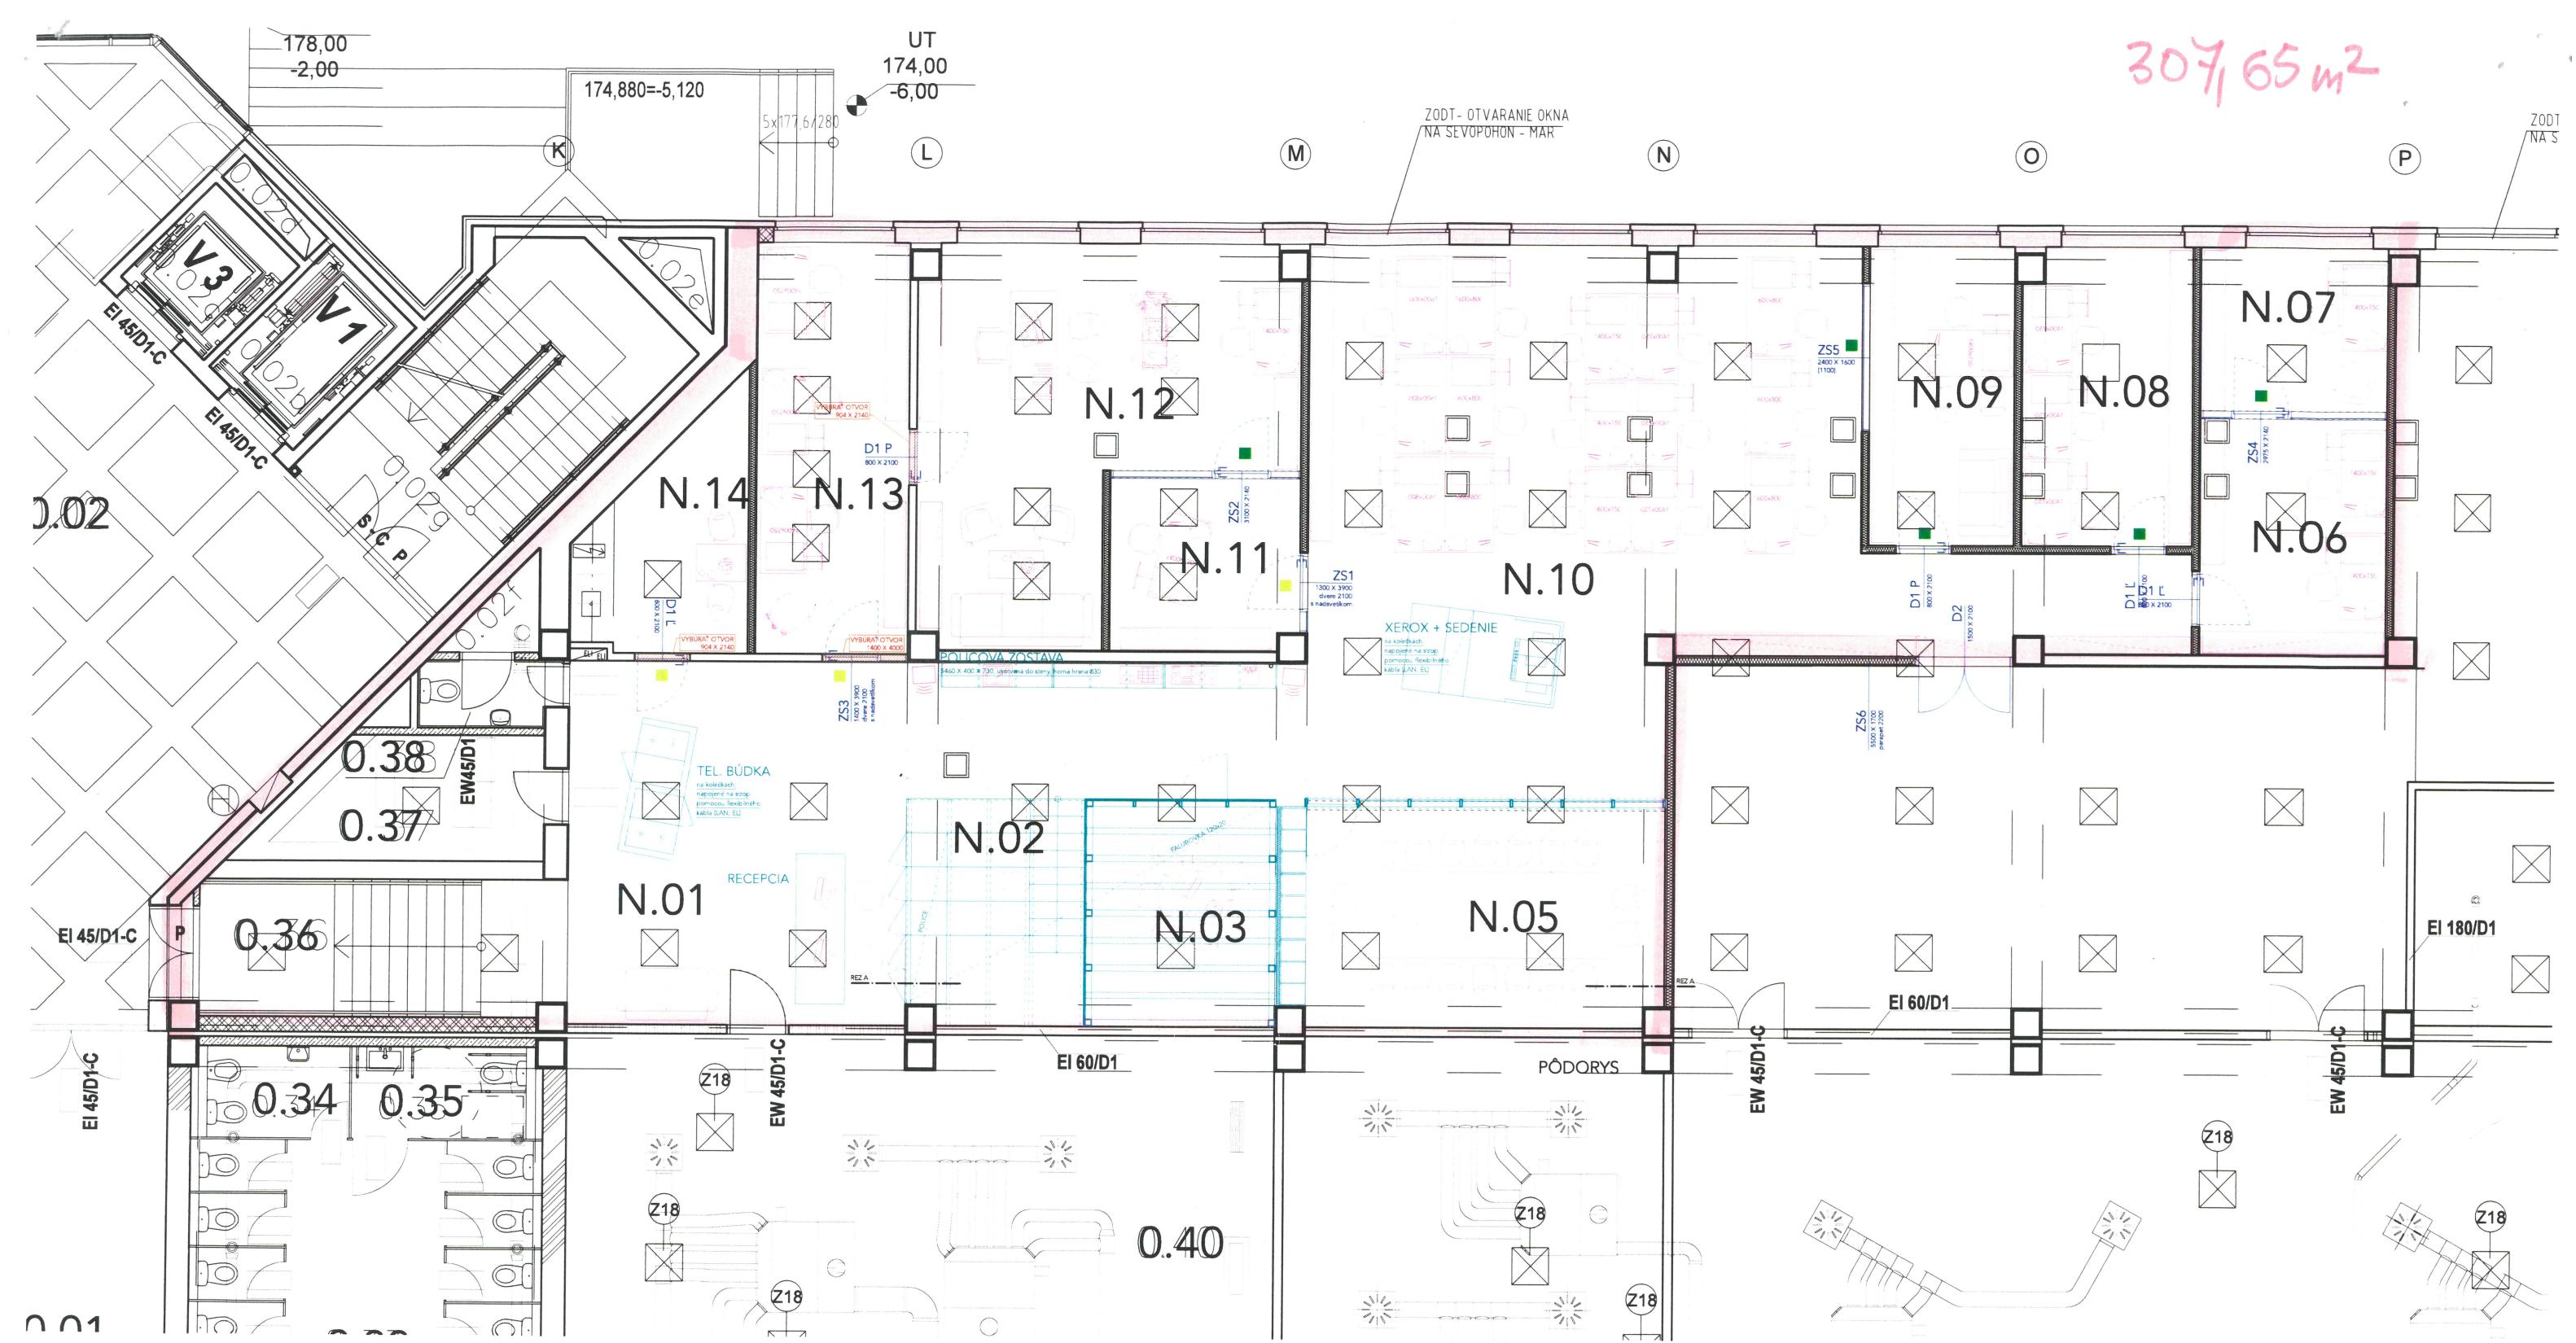

NOVÉ KANCELÁRSKE PRIESTORY

Č.M.	ÚČEL MIESTNOSTI	PLOCHA [m <sup>2</sup> ]	PODLAHA	STENY	STROPY	POZNÁMKA
N.01	RECEPCIA	32,57 m <sup>2</sup>	PVC + SOKLÍK	P1	SADROKARTÓN KAZETY V-3900 mm	
N.02	SCHODISKO	11,13 m <sup>2</sup>	PVC + SOKLÍK	P1	SADROKARTÓN KAZETY V-3900 mm	
N.03	PODSCHODISK.PRIESTOR (sklad)	11,00 m <sup>2</sup>	PVC + SOKLÍK	P1	TENKOVrstvová omietka + maľba OTERUVZDORNÁ	SADROKARTÓN KAZETY V-3900 mm
N.04	MALÁ ZASADAČKA	10,11 m <sup>2</sup>	PVC + SOKLÍK	P1	SADROKARTÓN KAZETY V-3900 mm	
N.05	VEĽKÁ ZASADAČKA	20,67 m <sup>2</sup>	KOBEREC	P2	SADROKARTÓN KAZETY V-3900 mm	
N.06	FINANČNÉ	11,05 m <sup>2</sup>	KOBEREC	P2	TENKOVrstvová omietka + maľba OTERUVZDORNÁ	SADROKARTÓN KAZETY V-3900 mm
N.07	FINANČNÉ	7,52 m <sup>2</sup>	KOBEREC	P2	TENKOVrstvová omietka + maľba OTERUVZDORNÁ	SADROKARTÓN KAZETY V-3900 mm
N.08	PRÁVNE	12,89 m <sup>2</sup>	KOBEREC	P2	TENKOVrstvová omietka + maľba OTERUVZDORNÁ	SADROKARTÓN KAZETY V-3900 mm
N.09	KANCELÁRIA	11,21 m <sup>2</sup>	KOBEREC	P2	TENKOVrstvová omietka + maľba OTERUVZDORNÁ	SADROKARTÓN KAZETY V-3900 mm
N.10	OPEN-SPACE	96,16 m <sup>2</sup>	KOBEREC	P2	TENKOVrstvová omietka + maľba OTERUVZDORNÁ	SADROKARTÓN KAZETY V-3900 mm
N.11	ASISTENTKA	8,45 m <sup>2</sup>	KOBEREC	P2	TENKOVrstvová omietka + maľba OTERUVZDORNÁ	SADROKARTÓN KAZETY V-3900 mm
N.12	KANCELÁRIA	30,54 m <sup>2</sup>	KOBEREC	P2	TENKOVrstvová omietka + maľba OTERUVZDORNÁ	SADROKARTÓN KAZETY V-3900 mm
N.13	KONZULTANTI	16,16 m <sup>2</sup>	KOBEREC	P2	TENKOVrstvová omietka + maľba OTERUVZDORNÁ	SADROKARTÓN KAZETY V-3900 mm
N.14	KUCHYNKA	9,15 m <sup>2</sup>	PVC + SOKLÍK	P1	TENKOVrstvová omietka + maľba OTERUVZDORNÁ	SADROKARTÓN KAZETY V-3900 mm

AUTOR	ING. ARCH. PETER JURKOVIČ	DÁTUM	04/2013
ZOD. PROJEKTANT	ING. F. SOLÁR	FORMÁT	2 x A4
VYPRACOVAL	ING. ARCH. PETER JURKOVIČ	MIERKA	1 : 100
INVESTOR		Č. VÝKRESU	A 02
NÁZOV	NOVÉ KANCELÁRSKE PRIESTORY	STUPEŇ PD	RP
MIESTO STAVBY	FIIT STU V BRATISLAVE	SADA	
STAVEBNÝ OBJEKT	SO 02.01 FAKULTA FIIT		
ČASŤ	ARCHITEKTÚRA		
OBSAH	PÔDORYS 1.PP — NÁVRH		